

DNK

ELECTRIC CIRCUIT DIAGRAM

유로계_압입전 LEAK TEST M/C

2025. 06. 14

PROJECT : 유로계_압입전 LEAK TEST M/C	제 도 DRAWN	설 계 DESIGN	검 도 CHECKED	승 인 APPROVED	 (주)대한콘트롤 Daehan Control
TITLE : MAIN TITLE	OH.J.H				
DATE : 2025. 06. 14	DWG NO. 100-01				

DNK
유로계_압입전 LEAK TEST M/C
ELECTRIC CIRCUIT DIAGRAM


I N D E X		
1	전개접속도 CIRCUIT DIAGRAM	0200 - 600
2	외관도 배치도 판금도 BOX DRAWING	0010 - 040
3	부품표 PART LIST	1100
4	명판 NAME PLATE	별지
5		
6		
7		

배선색	
교류전원·동력회로	흑색
어스선	녹/황
교류제어회로(단상)	적색
직류제어회로(단상)	청색
인터록 회로 공정간, 설비간 인터록 주차단기 일차측조명회로, 콘센트회로	황색
일반사용전선종류	체크
전원·동력회로	AWG(UL규격품)
제어회로	AWG(UL규격품)
마크 튜브	백색튜브/흑색문자
일반회로	백지/흑색문자
INTERLOCK회로	
절연튜브	
전원·동력회로	R상:적 S상: 황 T상:청


* Earth 배선시 단자간 Jump배선은 금지한다.
* Earth 배선시 earth배선 1단자에 단자 하나이다.
* Earth 배선시 여러개를 한묶음으로 단자 처리를 금지한다.
* Earth 배선시 earth단자 및 근방에 단자 처리한다.




자료체크

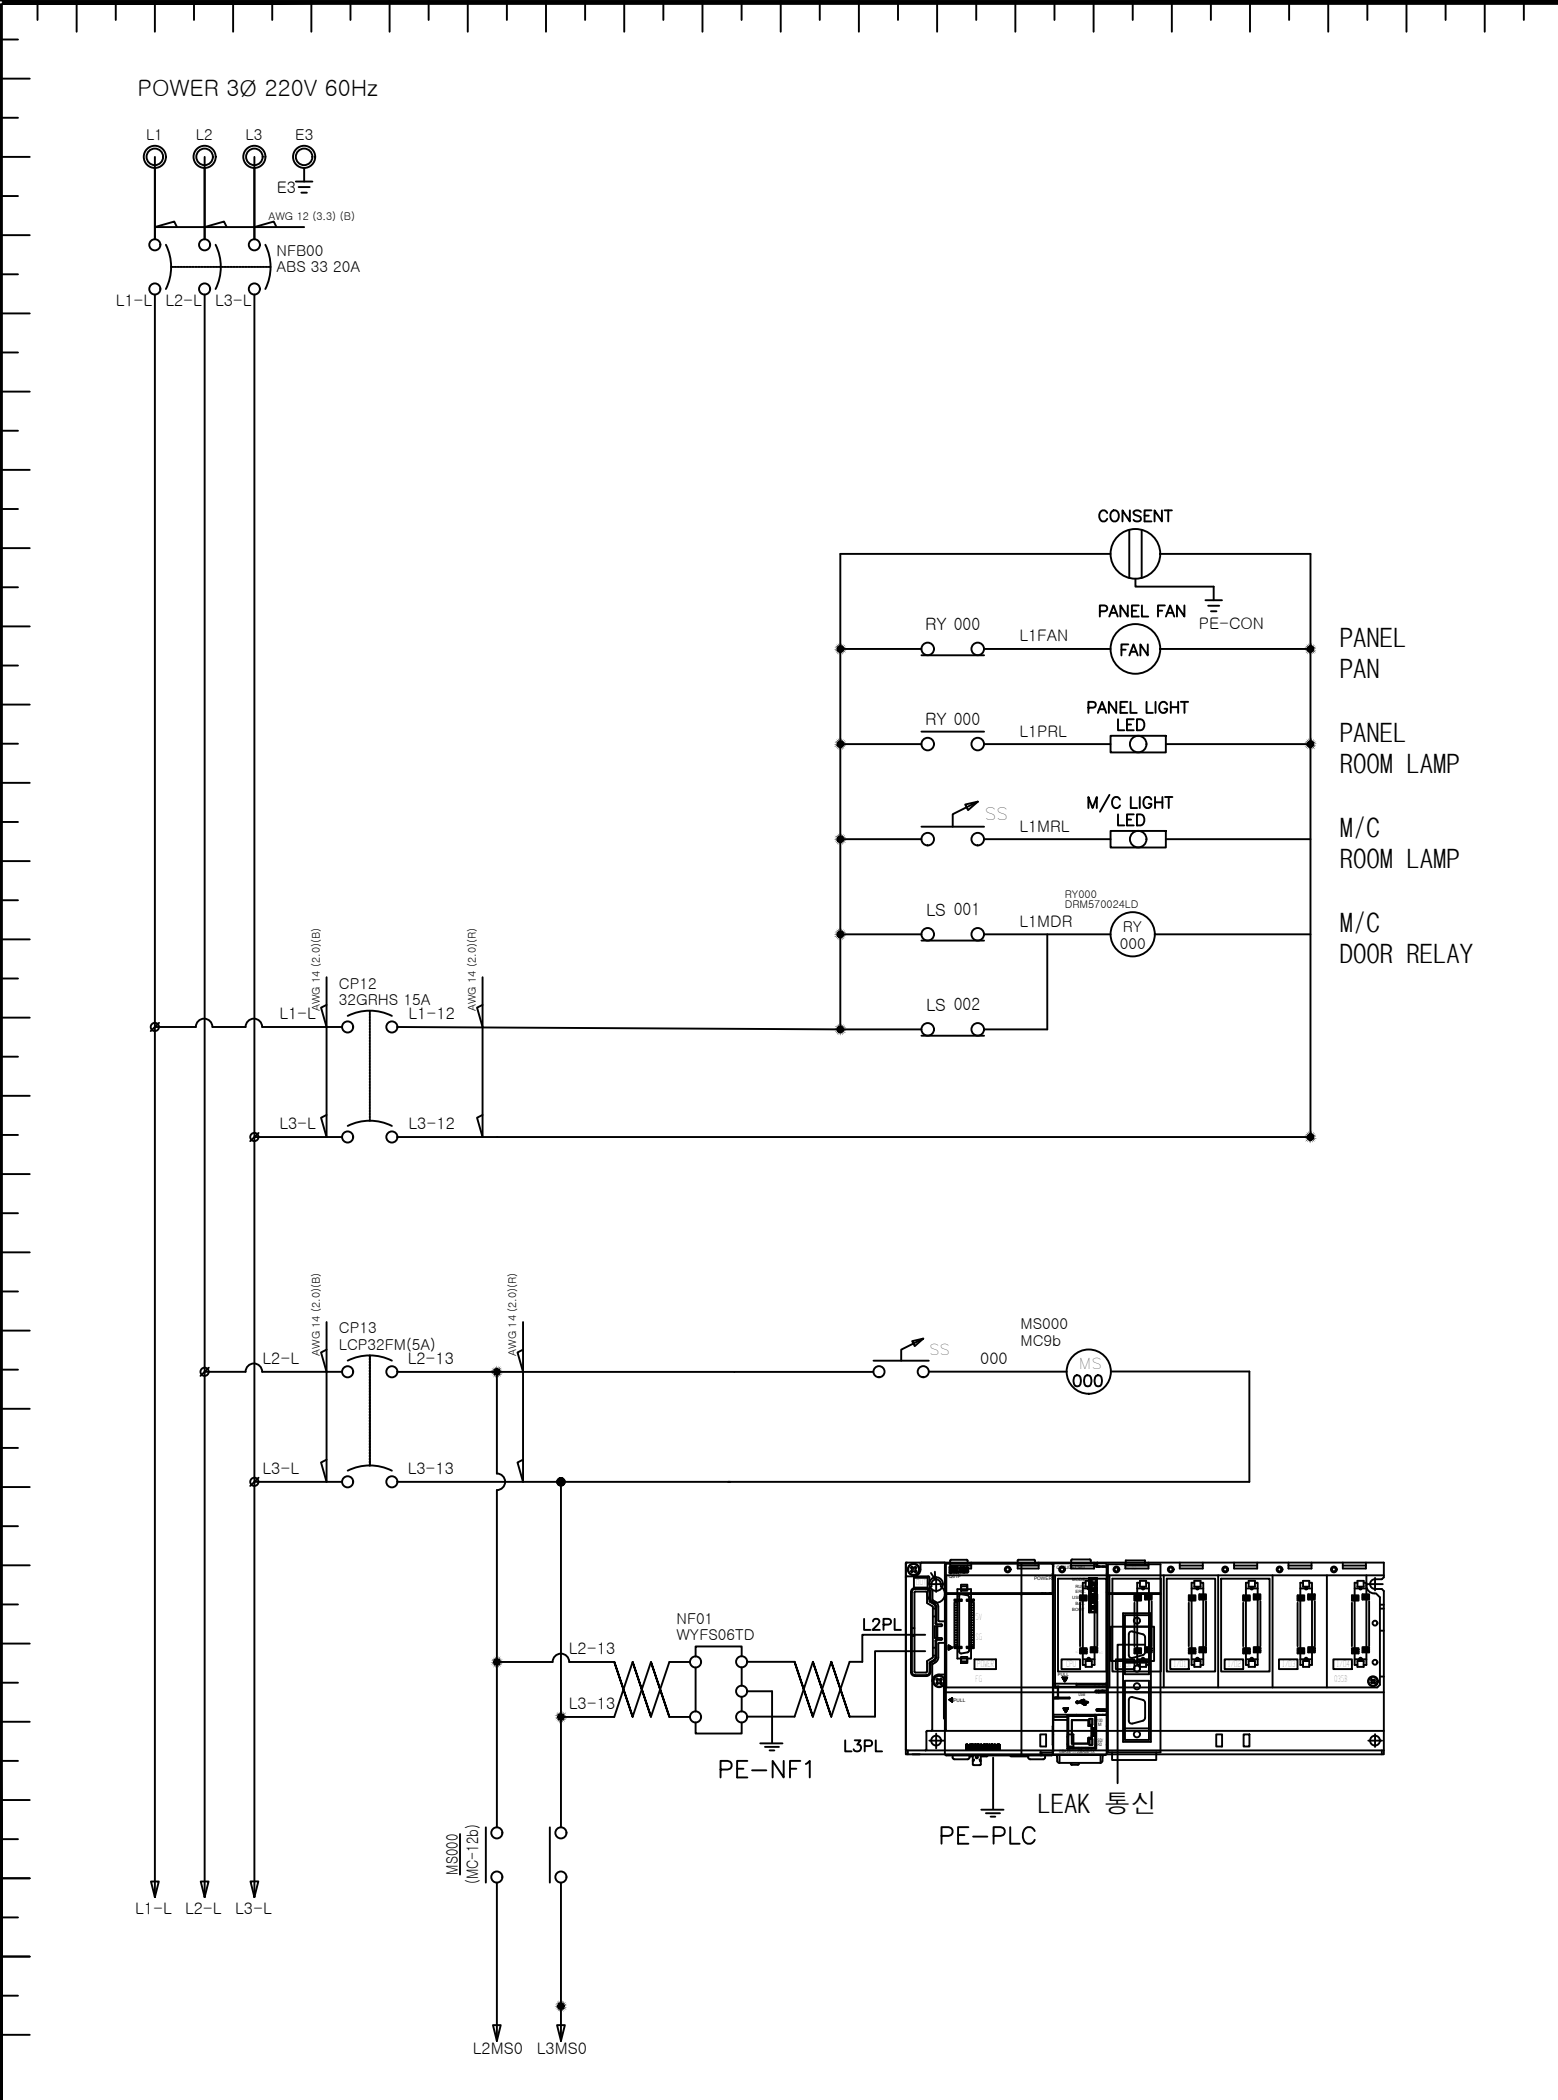


PROJECT : 유로계_압입전 LEAK TEST M/C	제 도 DRAWN	설 계 DESIGN	검 도 CHECKED	승 인 APPROVED	 (주)대한콘트롤 Daehan Control
TITLE : MAIN POWER & MOTOR POWER	OH.J.H				
DATE : 2025. 06. 14	DWG NO. 200-01				

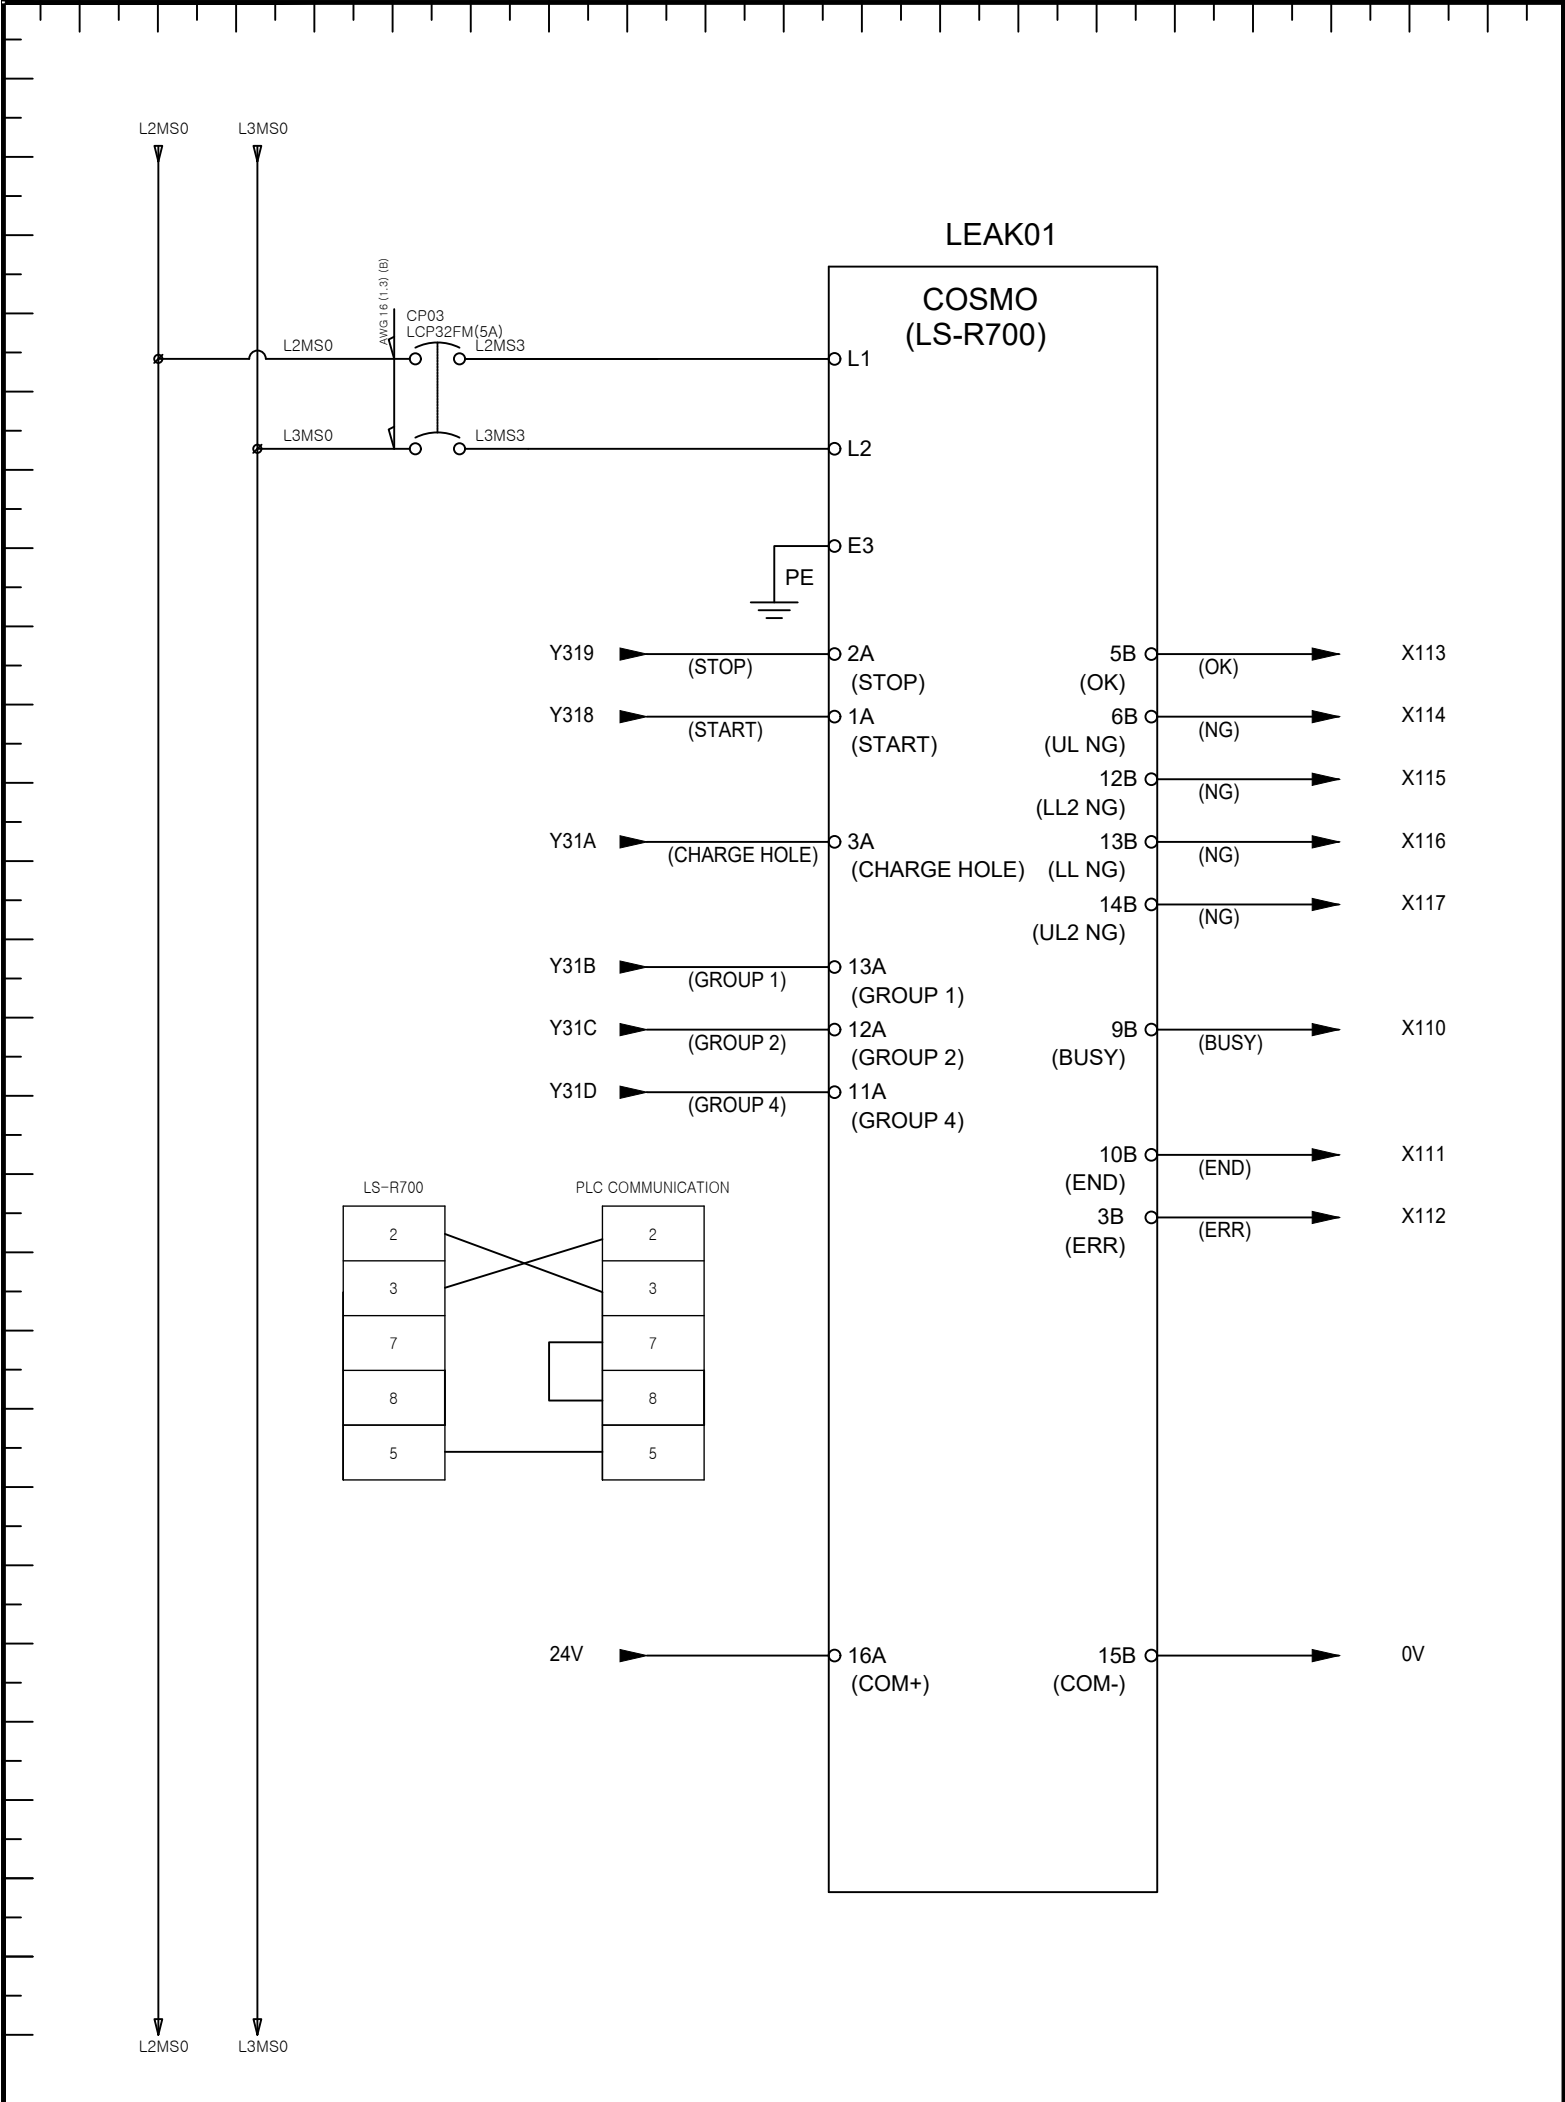

PROJECT :	제 도 DRAWN	설 계 DESIGN	검 도 CHECKED	승 인 APPROVED	 (주)대한컨트롤 <i>Daehan Control</i>
TITLE : CONTROL POWER	OH.J.H				
DATE : 2025. 06. 14	DWG NO. 200-02				

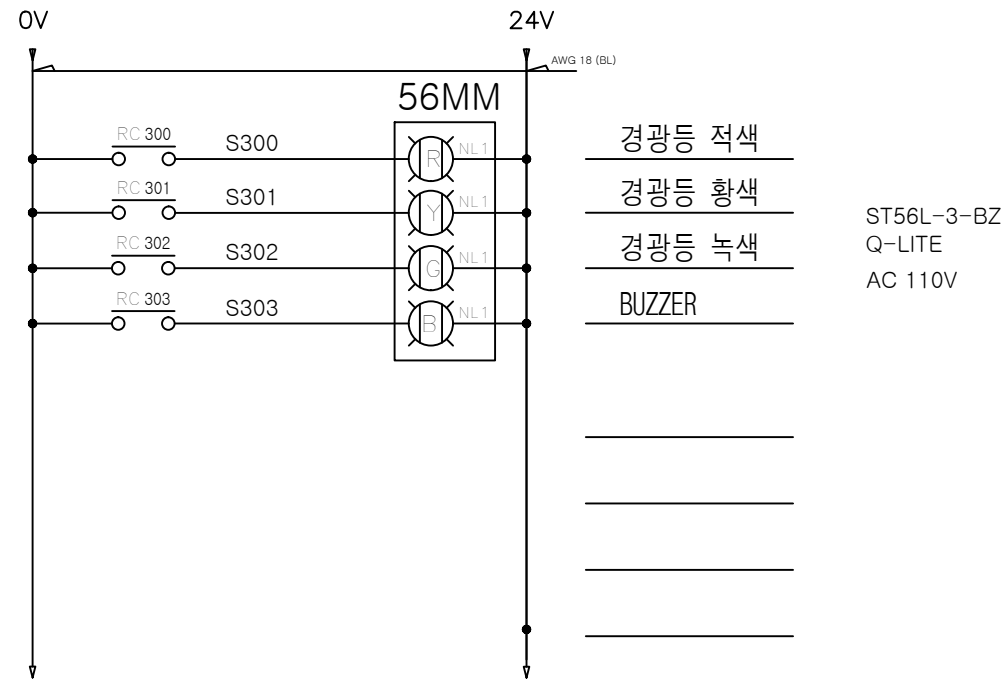


PLC<>MARKING

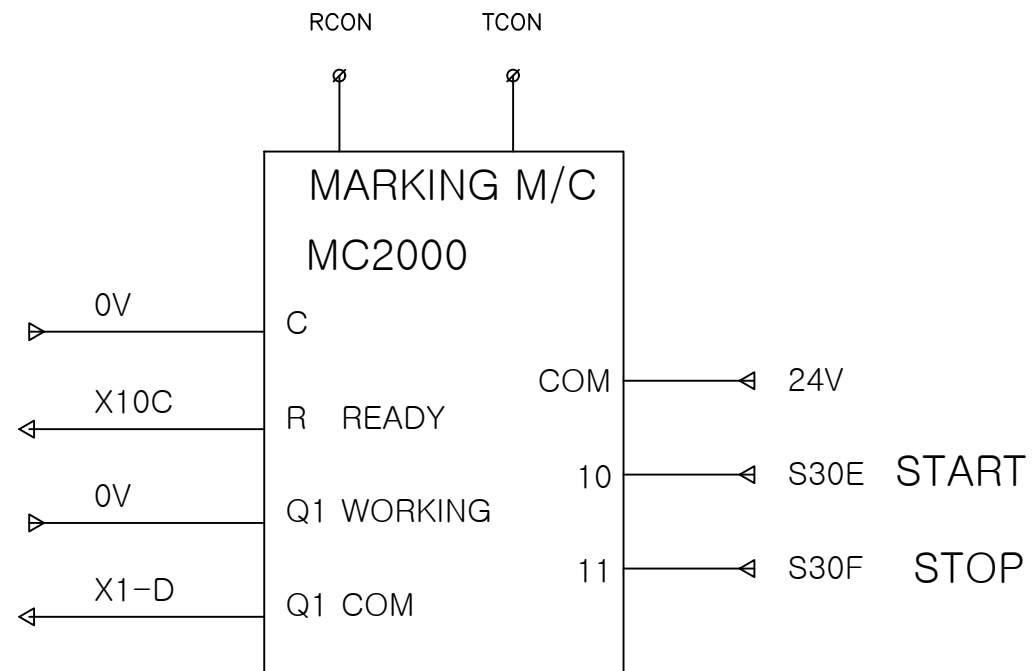

PLC<---> READING PLC I/O KEYENCE READING

IN	X109		READING OK	OUT 1	PINK
IN	X10A		READING NG	OUT 2	SKY BLUE
IN	X10B		READING READY	OUT 3	WHITE
COM	0V		OUTCOM	OUTCOM	BLACK
COM	0V		INCOM	INCOM	W/B
OUT	S30C		READING START	IN 1	GREEN
OUT	---		READING SPARE	IN 2	GRAY
				24V	BROWN
				0V	BLUE

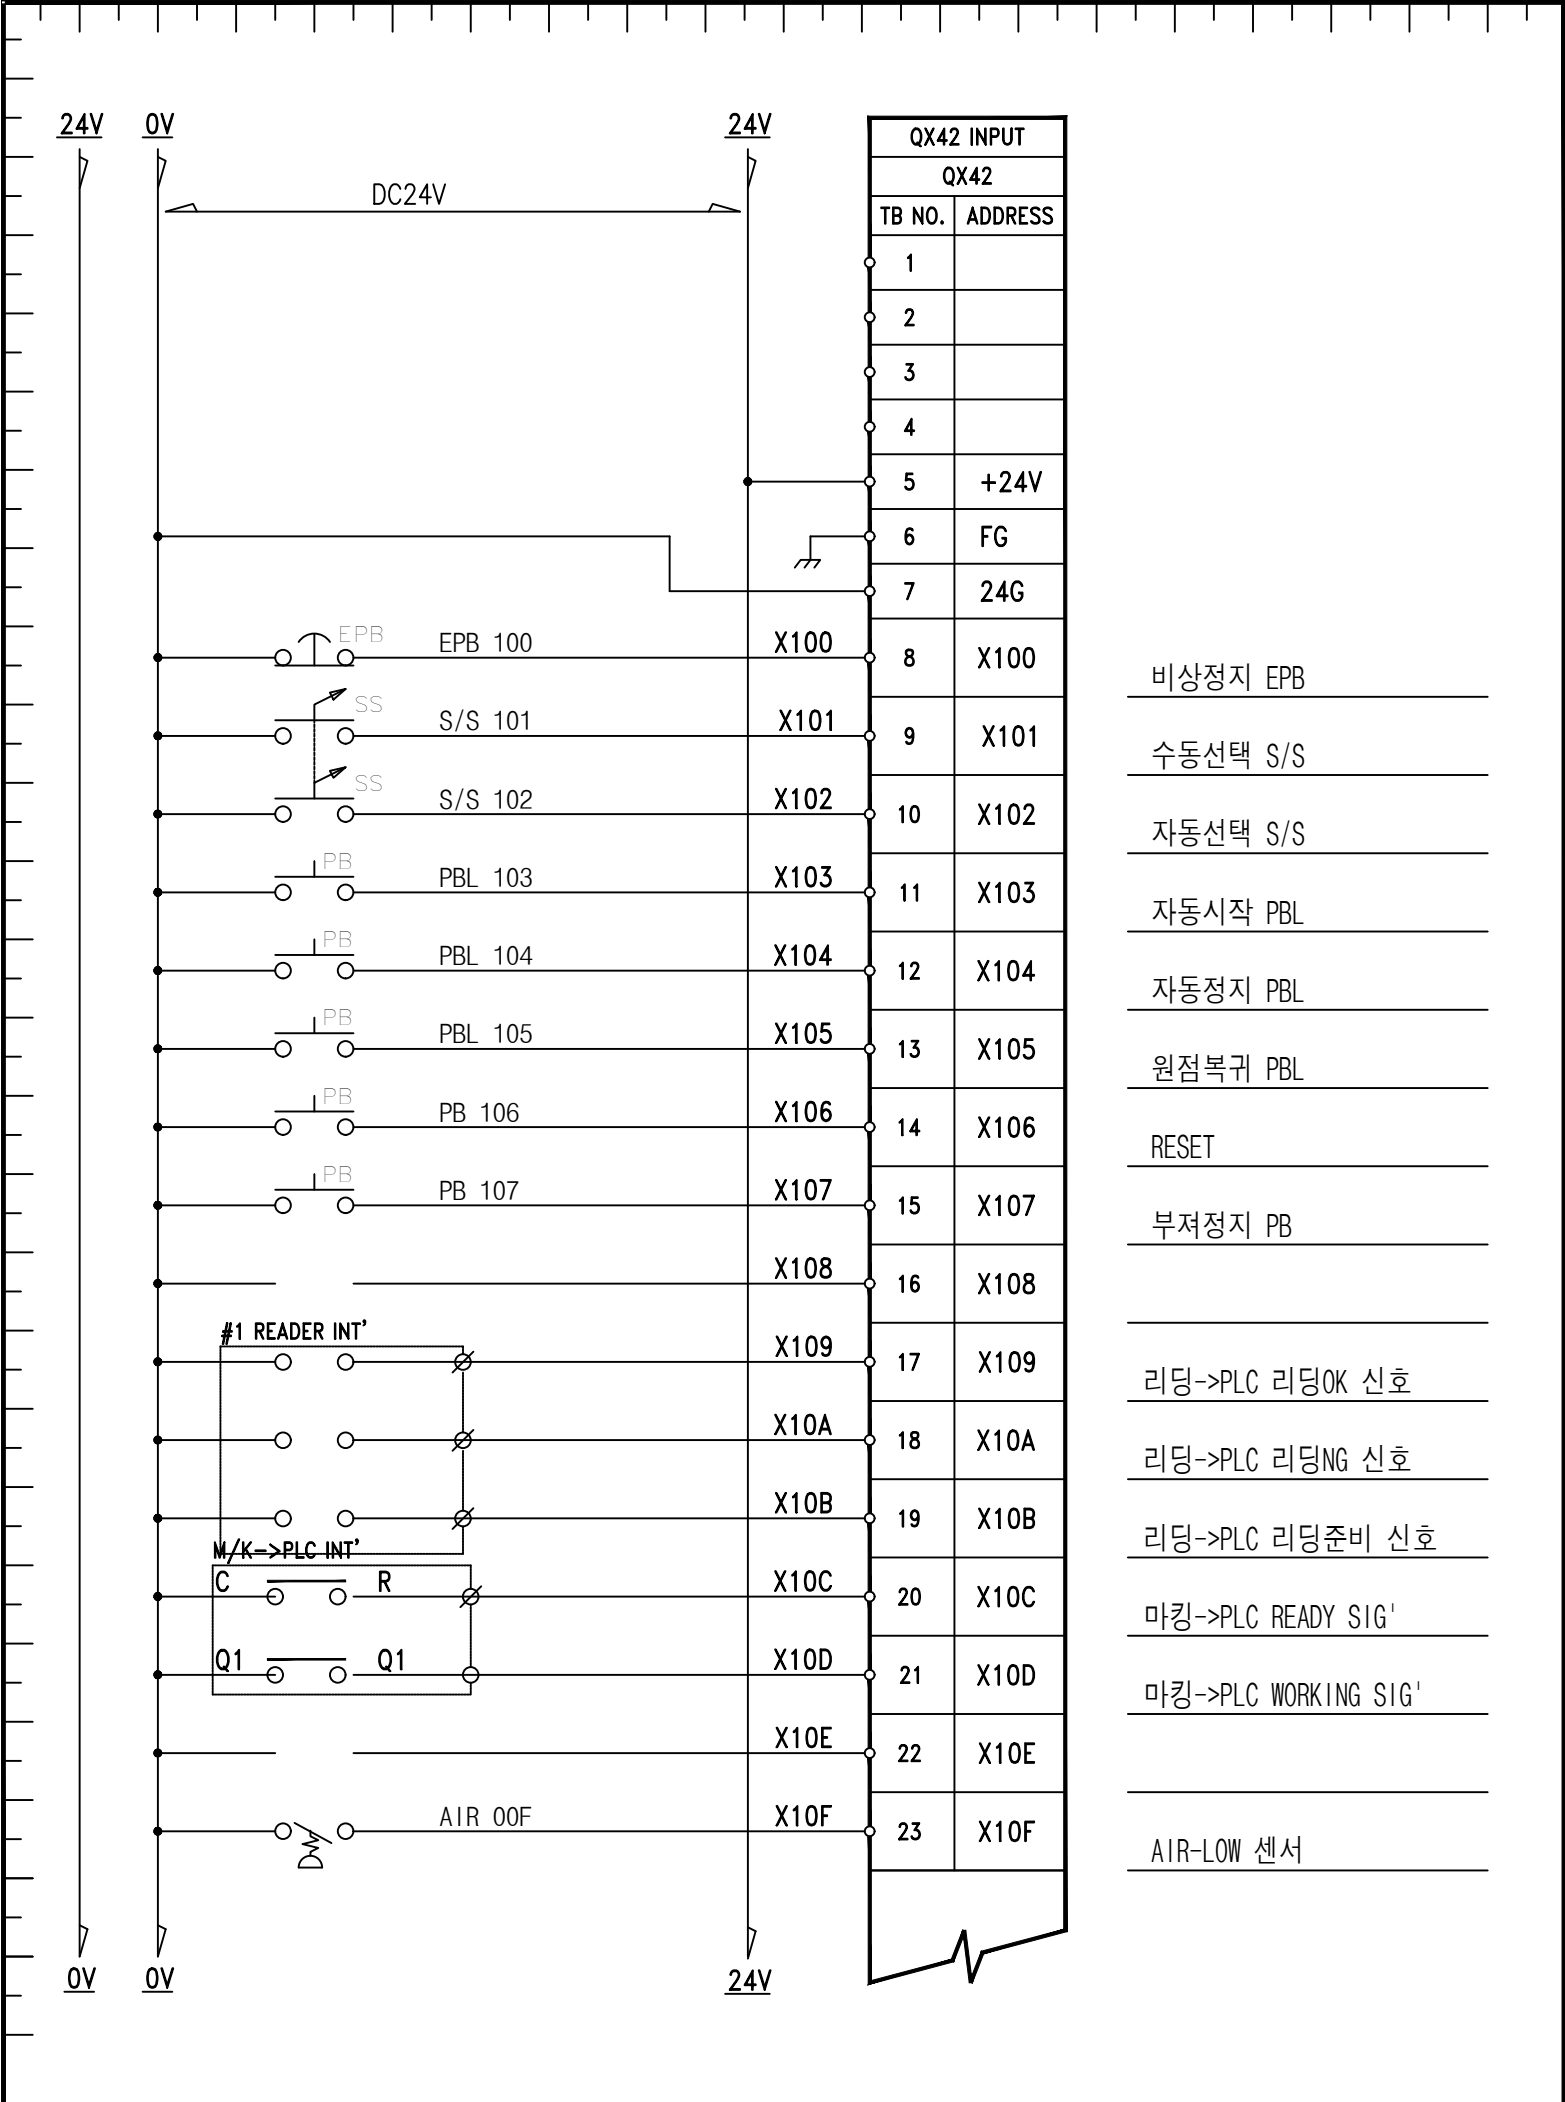

비상정지 EPB

수동선택 S/S

자동선택 S/S

자동시작 PBL

자동정지 PBL

원점복귀 PBL

RESET

부저정지 PB

리딩->PLC 리딩OK 신호


리딩->PLC 리딩NG 신호


리딩->PLC 리딩준비 신호

마킹->PLC READY SIG'


마킹->PLC WORKING SIG'


AIR-LOW 센서

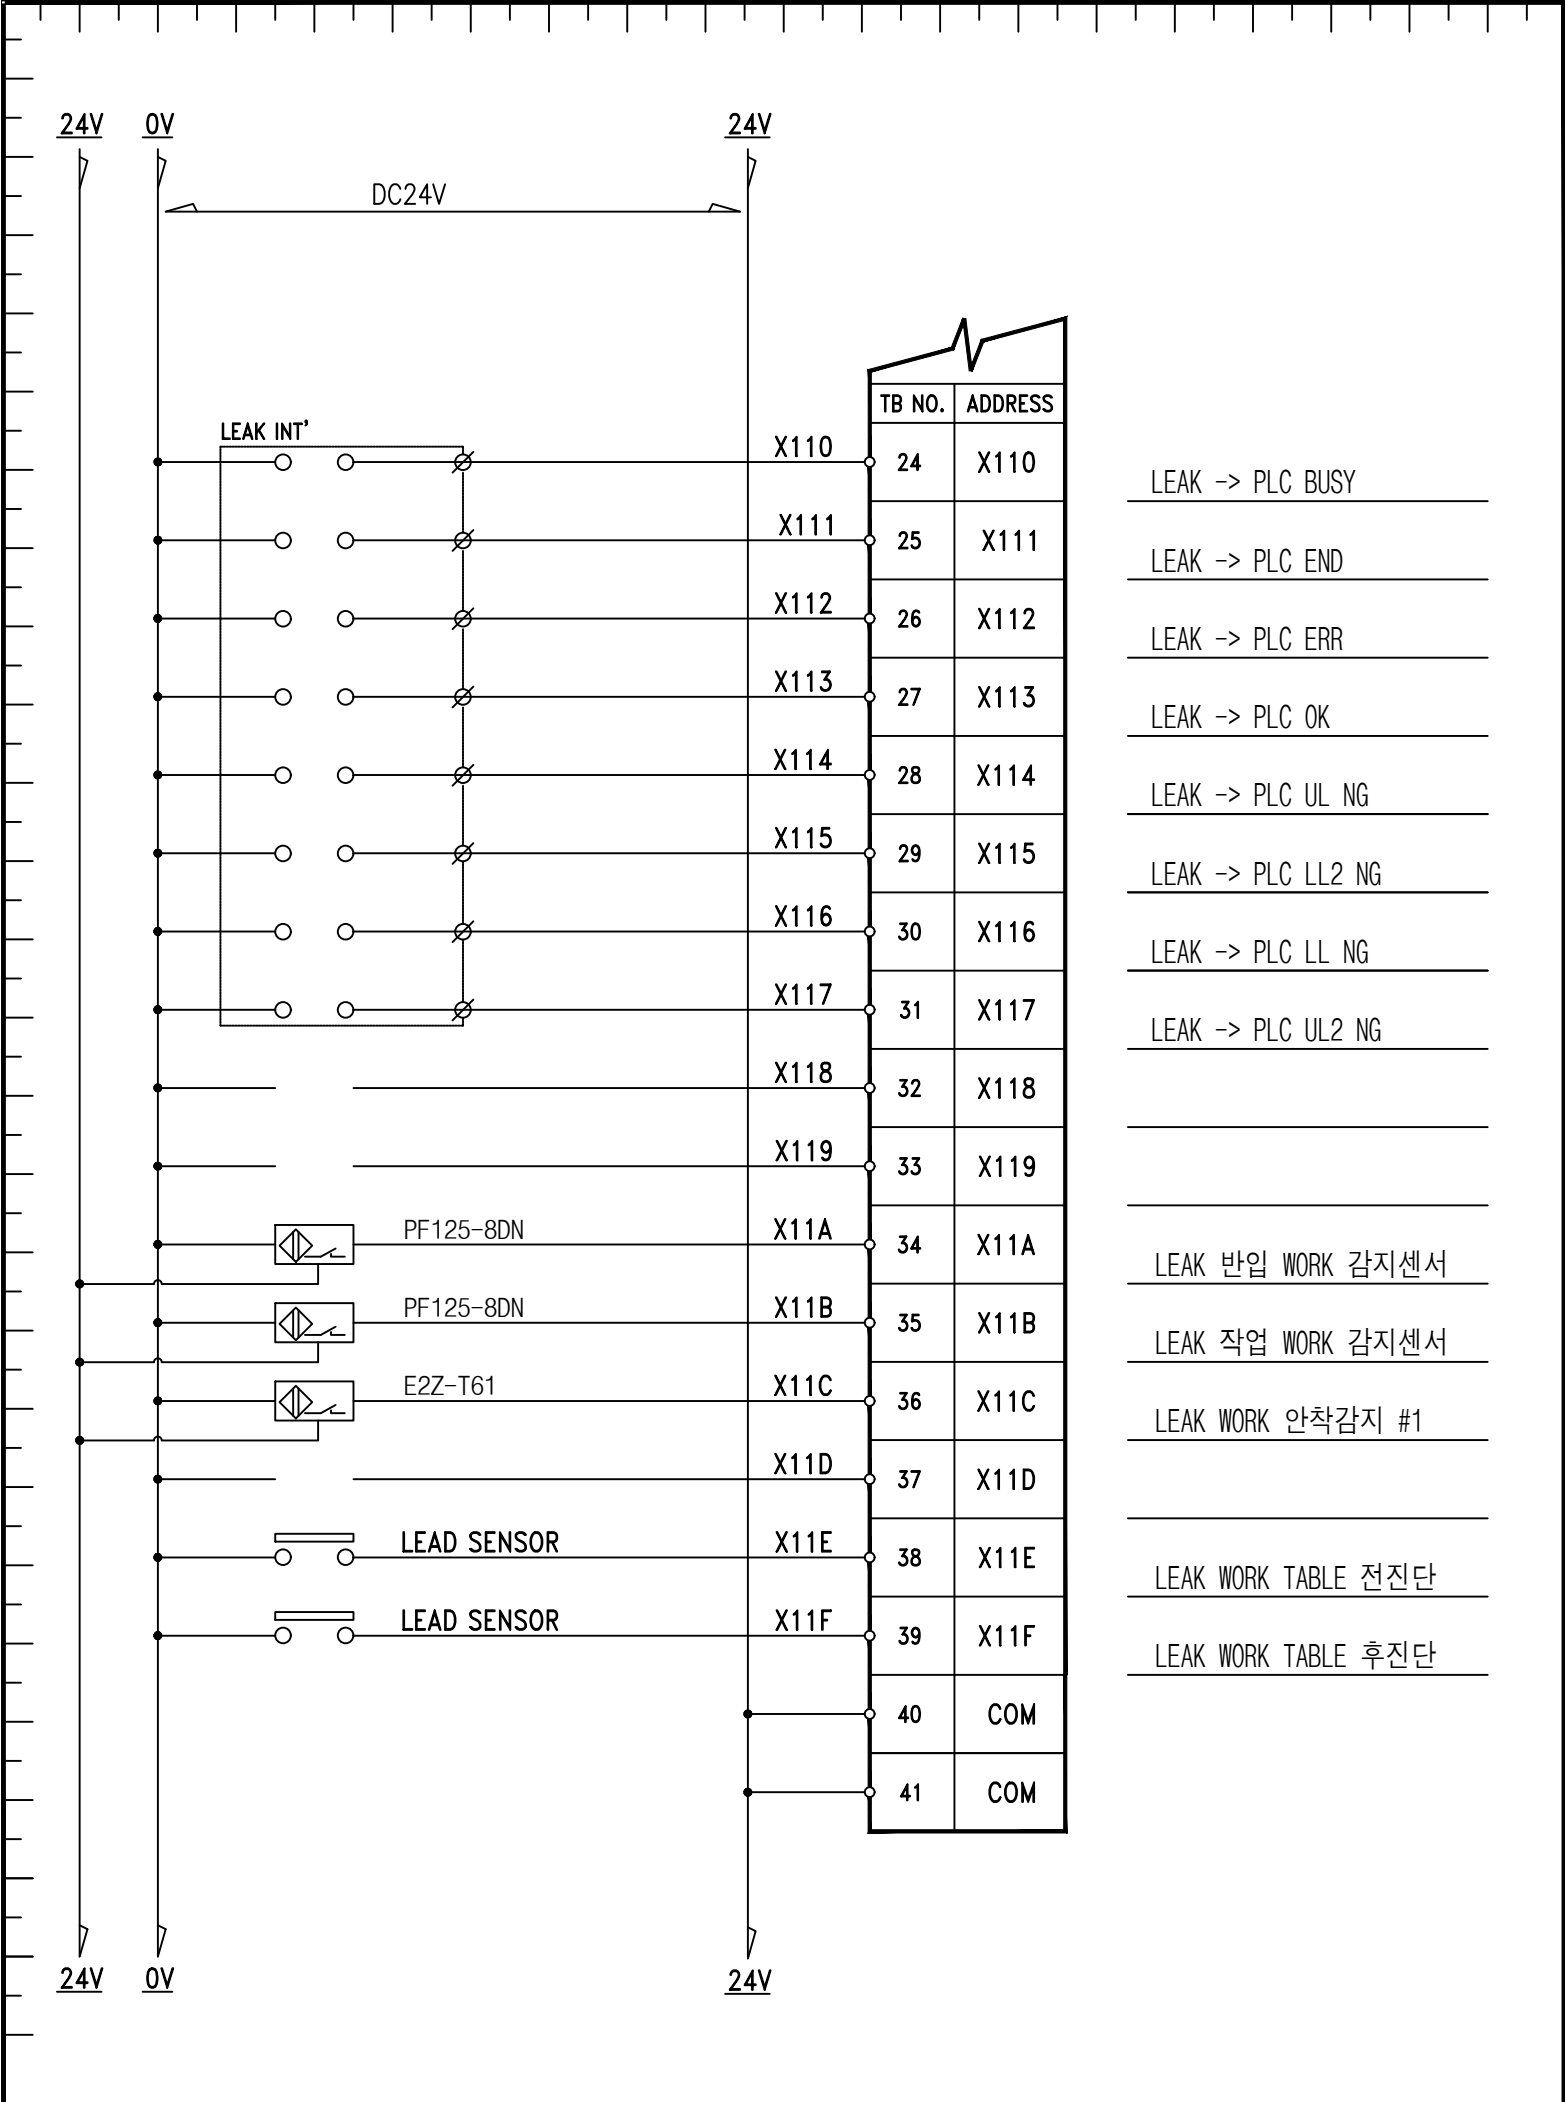

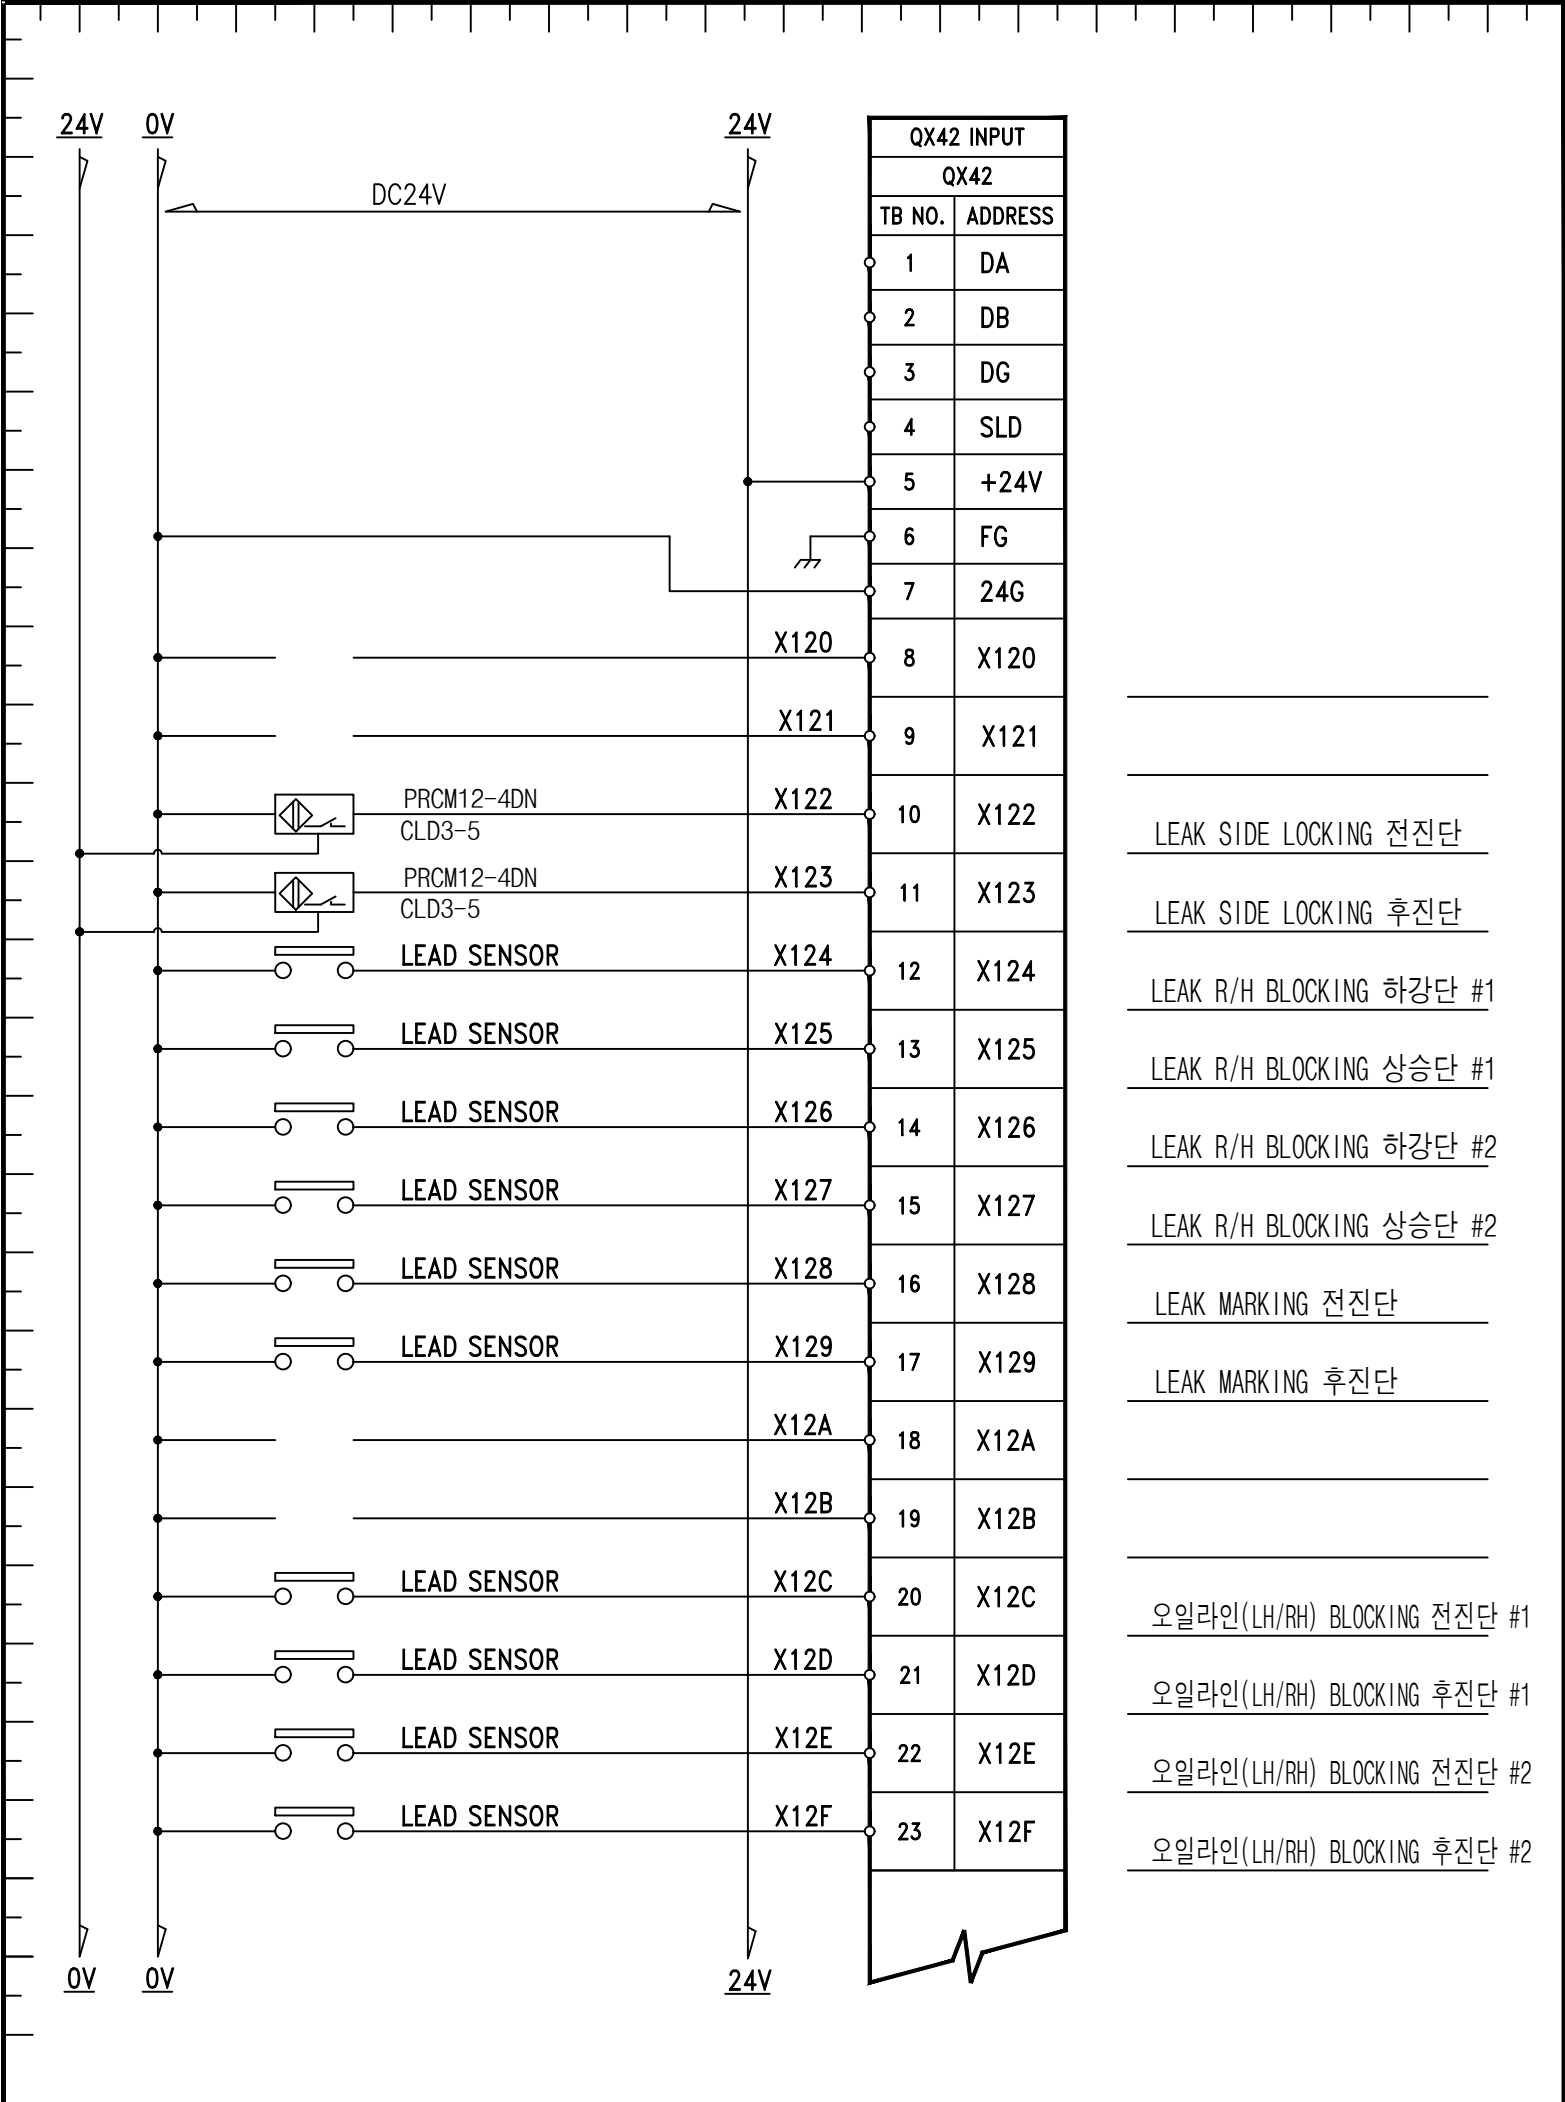

- LEAK SIDE LOCKING 전진단
- LEAK SIDE LOCKING 후진단
- LEAK R/H BLOCKING 하강단 #1
- LEAK R/H BLOCKING 상승단 #1
- LEAK R/H BLOCKING 하강단 #2
- LEAK R/H BLOCKING 상승단 #2
- LEAK MARKING 전진단
- LEAK MARKING 후진단
- 오일라인(LH/RH) BLOCKING 전진단 #1
- 오일라인(LH/RH) BLOCKING 후진단 #1
- 오일라인(LH/RH) BLOCKING 전진단 #2
- 오일라인(LH/RH) BLOCKING 후진단 #2

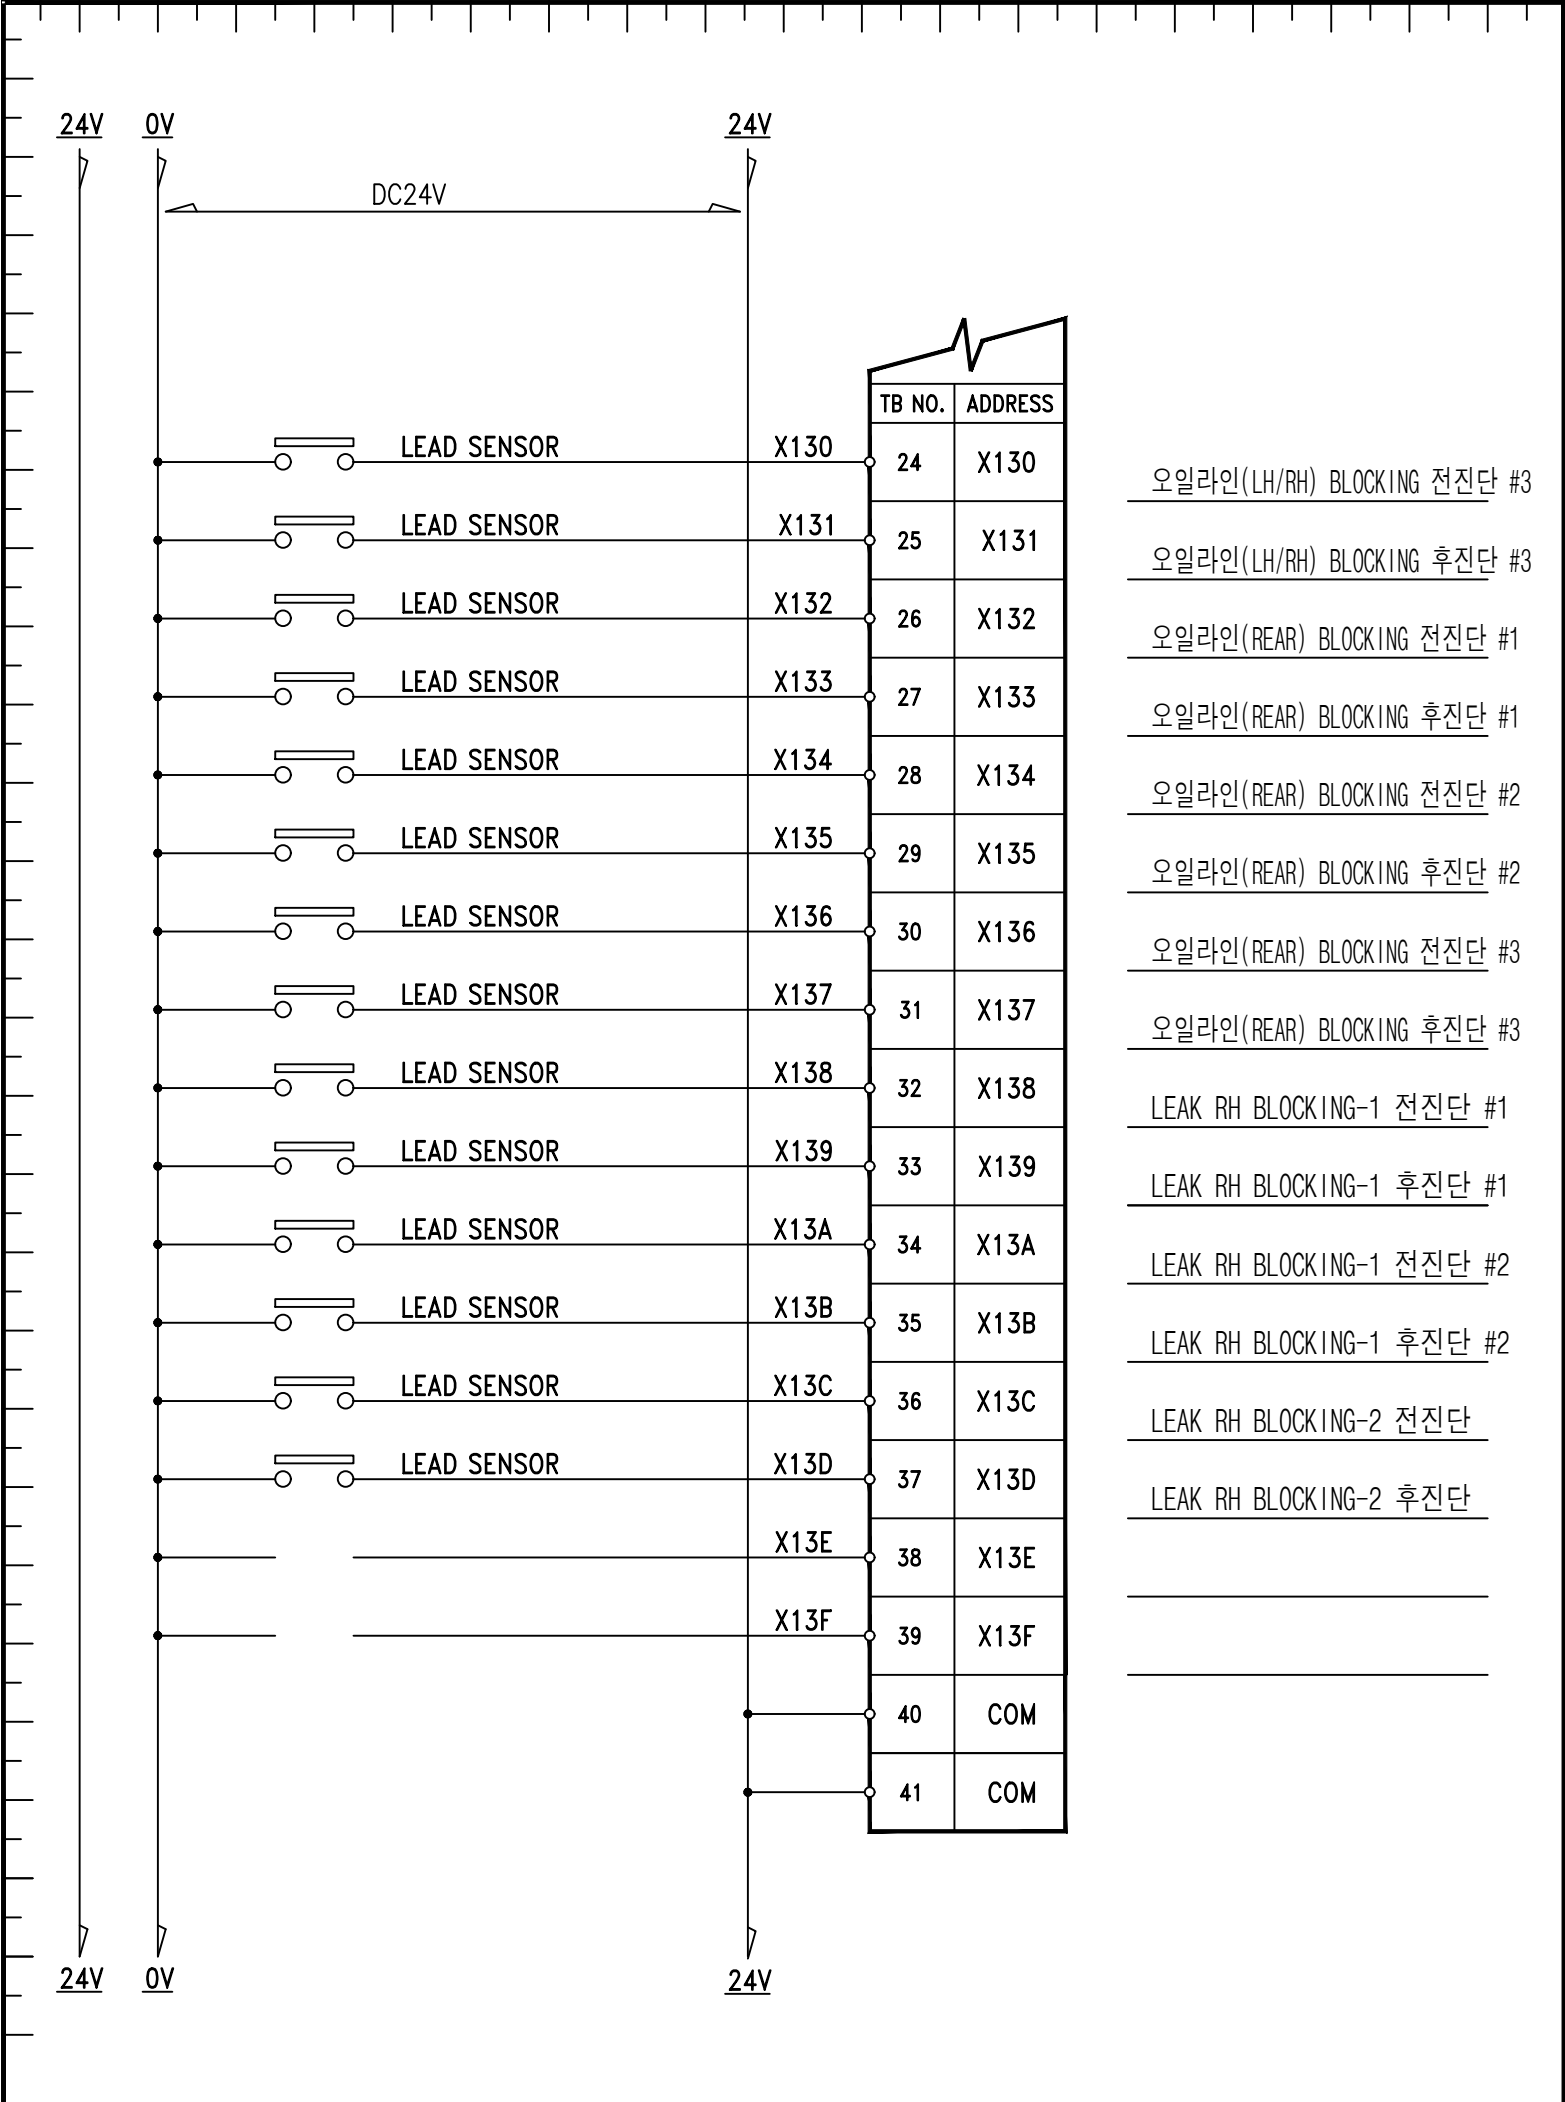

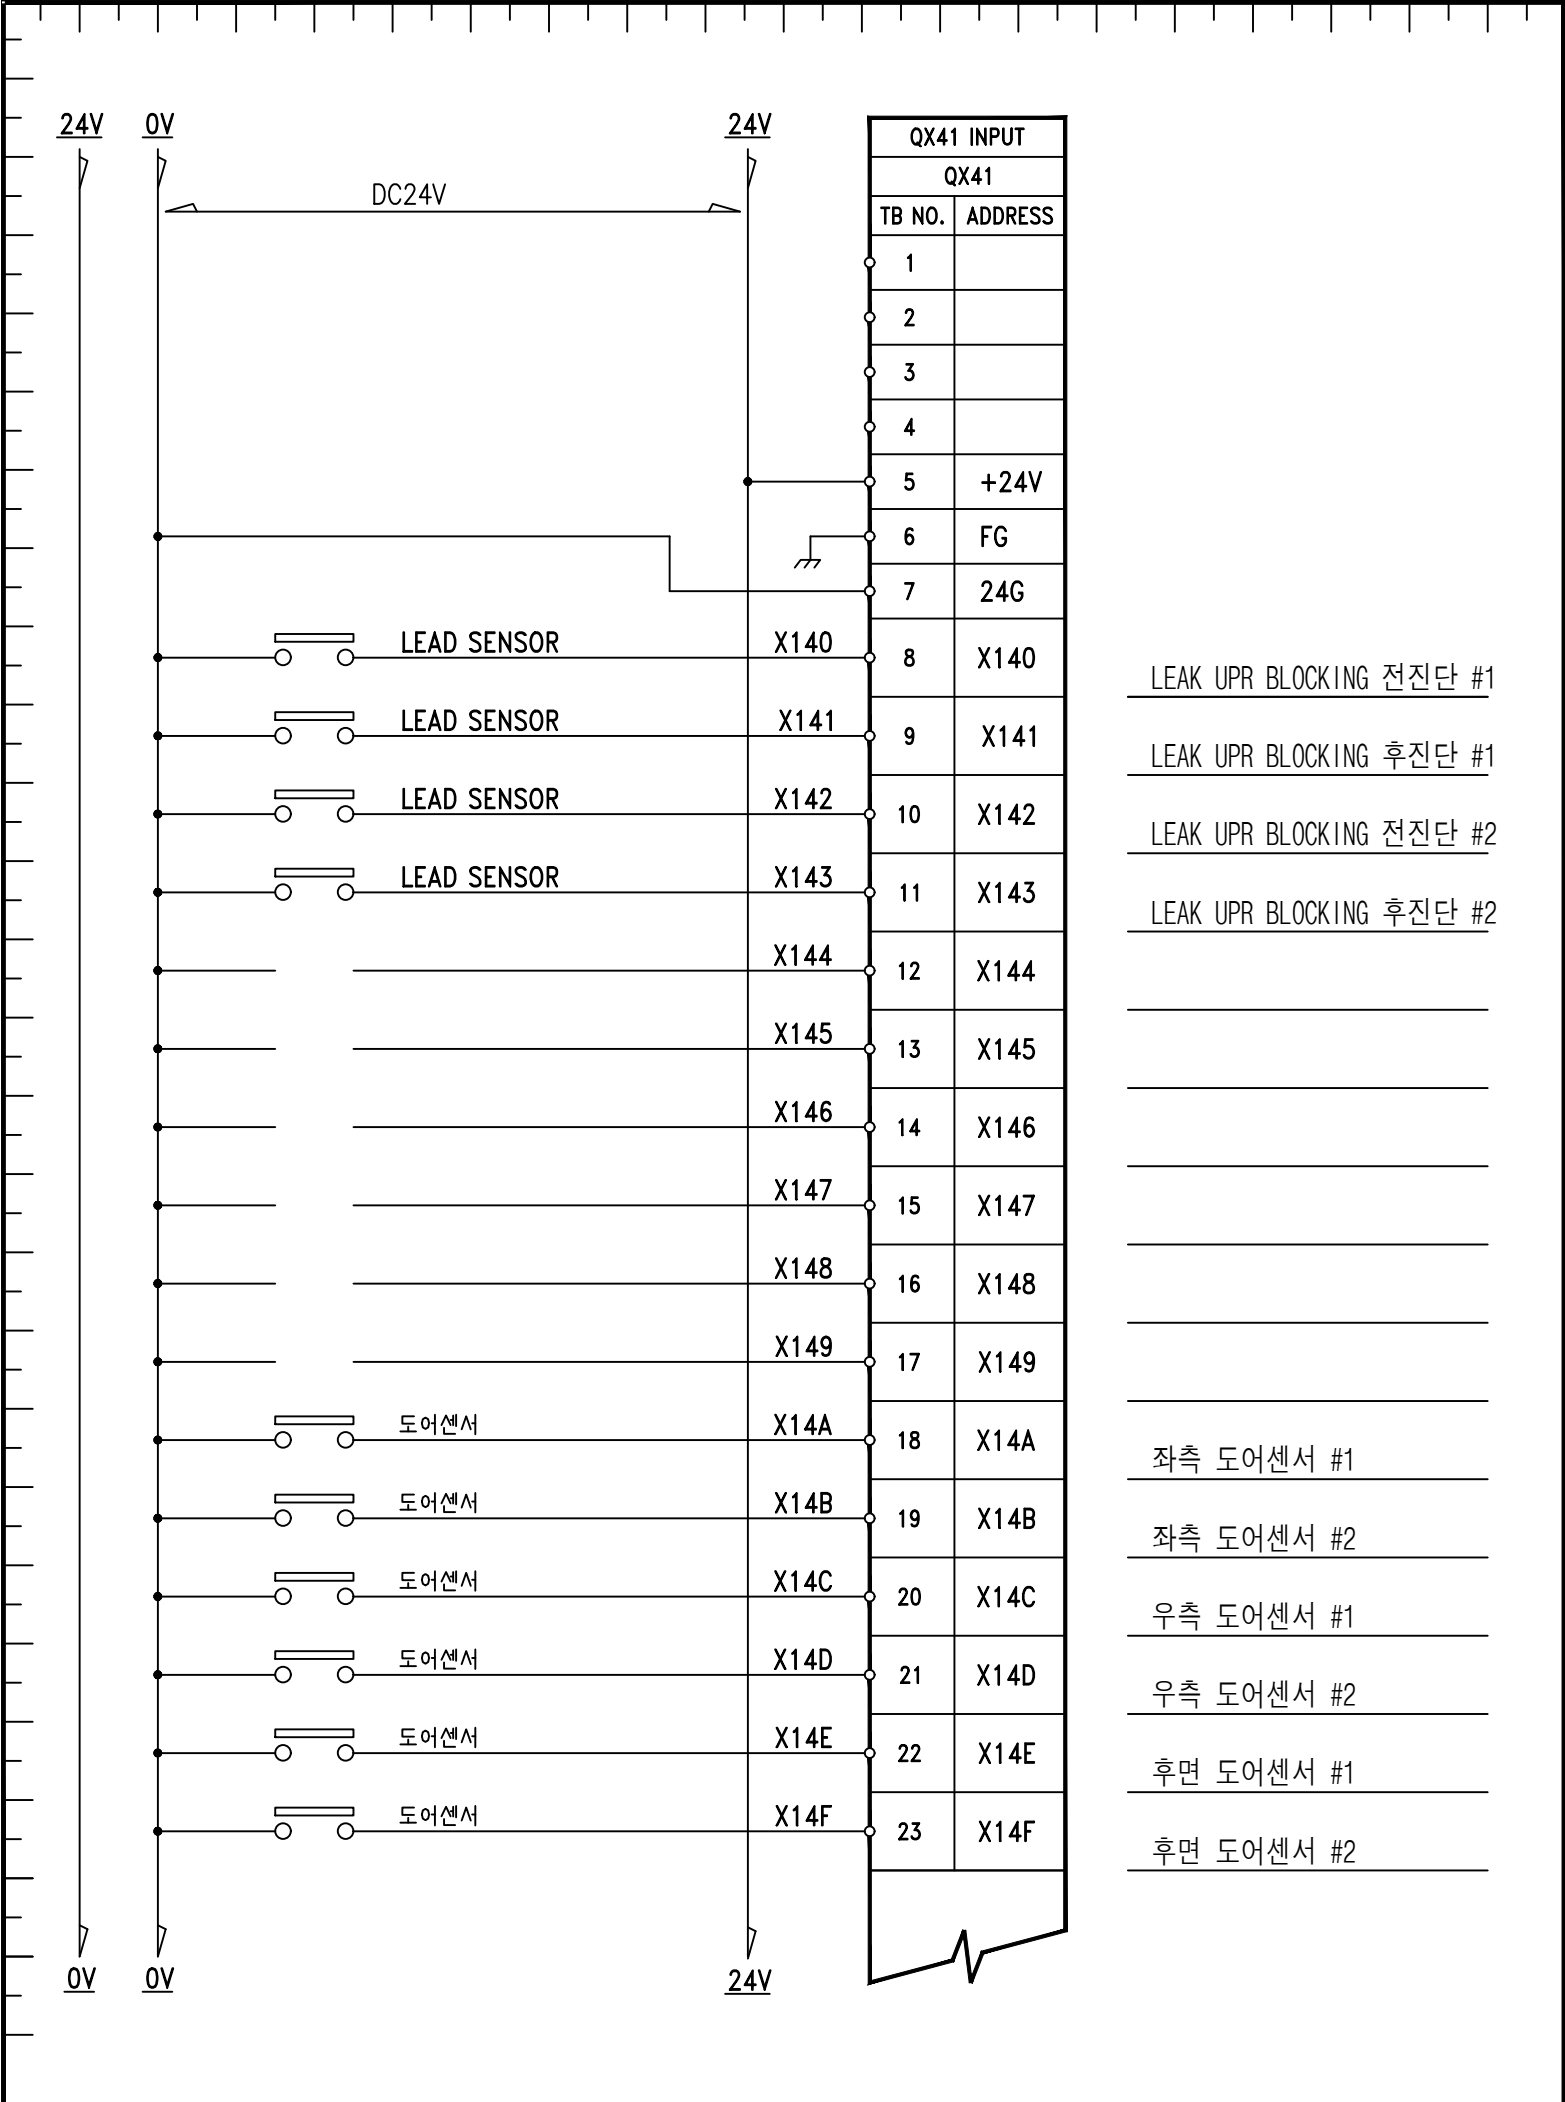

LEAK UPR BLOCKING 전진단 #1

LEAK UPR BLOCKING 후진단 #1

LEAK UPR BLOCKING 전진단 #2

LEAK UPR BLOCKING 후진단 #2

좌측 도어센서 #1

좌측 도어센서 #2


우측 도어센서 #1

우측 도어센서 #2

후면 도어센서 #1

후면 도어센서 #2

QY42P OUTPUT	
QY42P	
ADDRESS	TB NO.
	1
	2
	3
	4
+24V	5
FG	6
24G	7
Y300	8
Y301	9
Y302	10
Y303	11
Y304	12
Y305	13
Y306	14
Y307	15
Y308	16
Y309	17
Y30A	18
Y30B	19
Y30C	20
Y30D	21
Y30E	22
Y30F	23

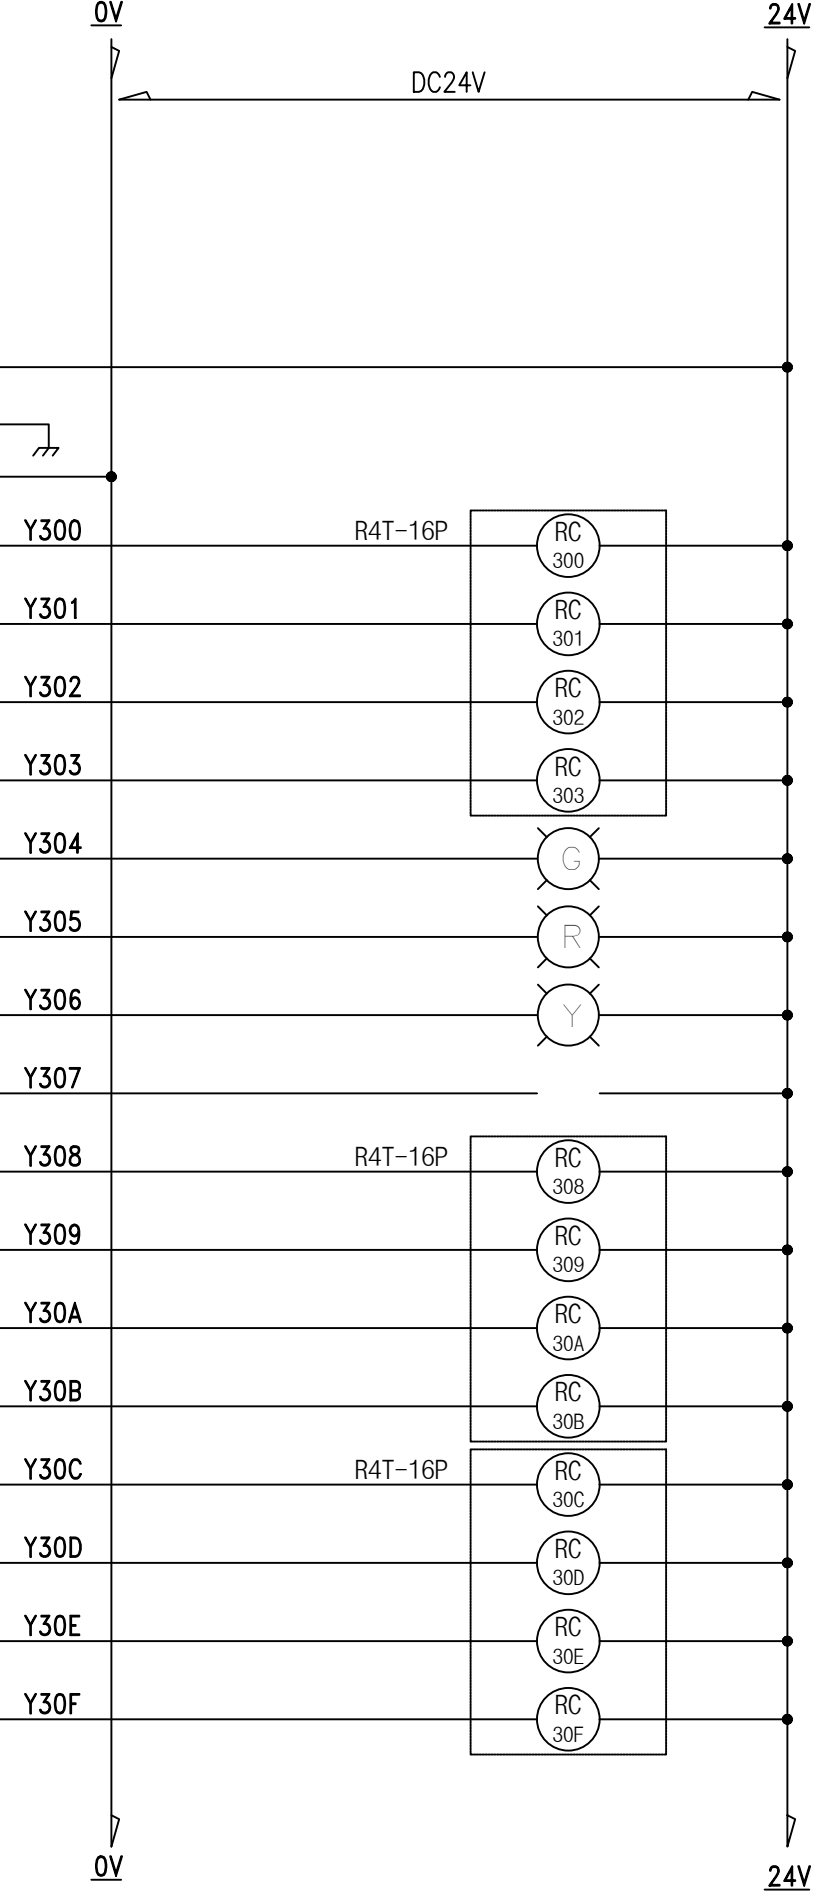

경광등 적색 램프

경광등 황색 램프

경광등 녹색 램프

부저

자동운전 OP 램프

자동정지 OP 램프


원점복귀 OP 램프

PLC -> READER TRIGGER

PLC->마킹 START 08 C=24V

PLC->마킹 STOP 11

QY42P OUTPUT	
QY42P	
ADDRESS	TB NO.
	1
	2
	3
	4
+24V	5
FG	6
24G	7
Y320	8
Y321	9
Y322	10
Y323	11
Y324	12
Y325	13
Y326	14
Y327	15
Y328	16
Y329	17
Y32A	18
Y32B	19
Y32C	20
Y32D	21
Y32E	22
Y32F	23

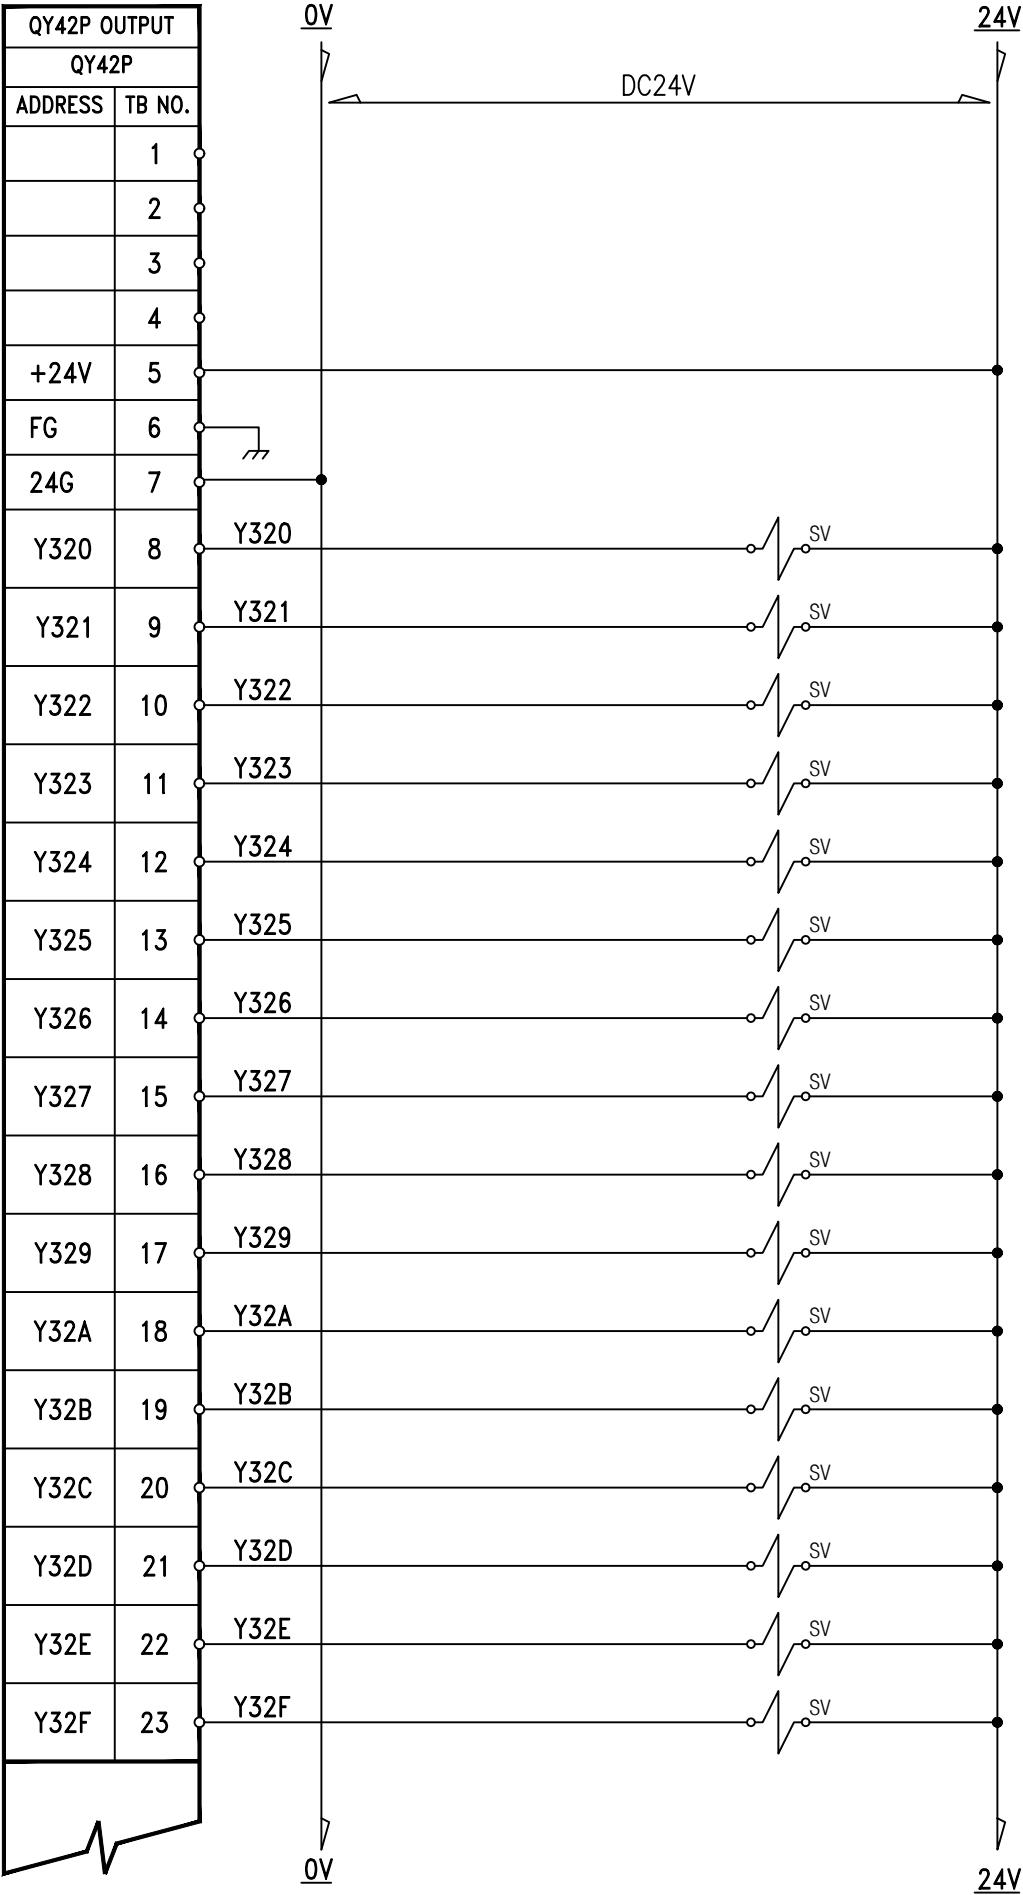

WORK TABLE 전진_SOL

WORK TABLE 후진_SOL

LEAK SIDE LOCKING 전진_SOL

LEAK SIDE LOCKING 후진_SOL

LEAK R/H BLOCKING 하강_SOL

LEAK R/H BLOCKING 상승_SOL

LEAK MARKING 전진_SOL

LEAK MARKING 후진_SOL

LEAK BOOSTER 하강_SOL

LEAK BOOSTER 상승_SOL

오일라인(LH/RH) BLOCKING 전진_SOL

오일라인(LH/RH) BLOCKING 후진_SOL

오일라인(REAR) BLOCKING 전진_SOL

오일라인(REAR) BLOCKING 후진_SOL

LEAK AIR BLOW ON_SOL

PROJECT : 유로계_압입전 LEAK TEST M/C

TITLE : PLC OUTPUT Y320~Y32F CIRCUIT

DATE : 2025. 06. 14

제 도

DRAWN

설 계

DESIGN

OH J.H

DWG NO. 400-03

검 도

CHECKED


승 인

APPROVED



(주)대한콘트롤

Daehan Control

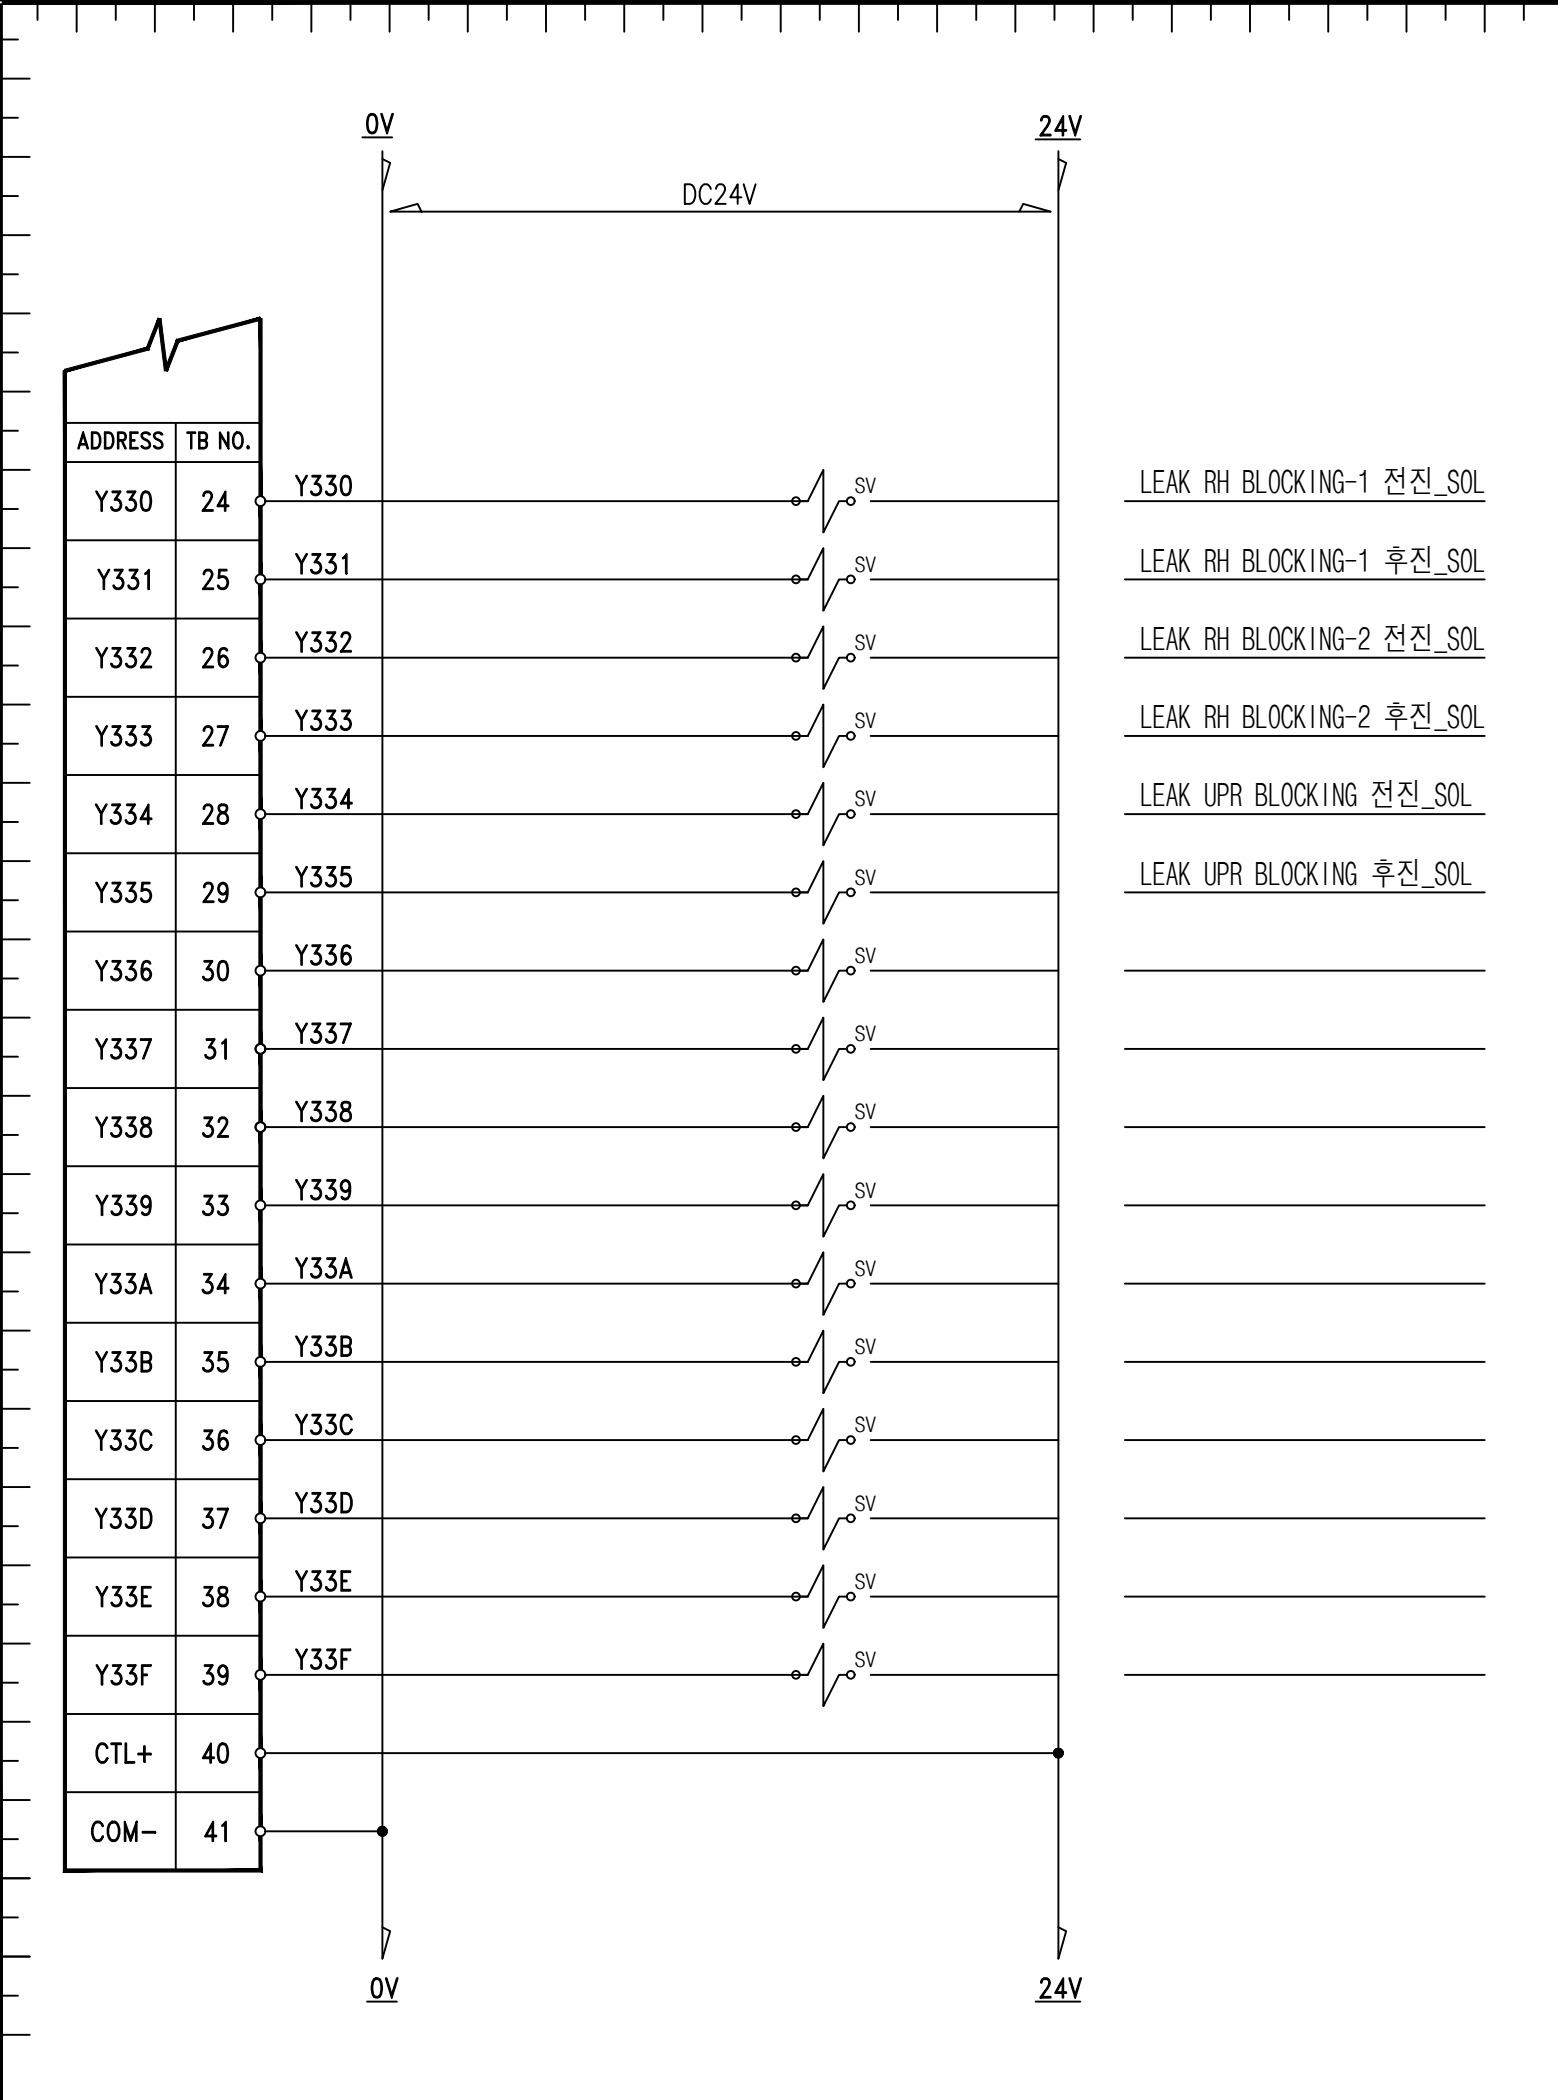

LEAK RH BLOCKING-1 전진_SOL

LEAK RH BLOCKING-1 후진_SOL

LEAK RH BLOCKING-2 전진_SOL

LEAK RH BLOCKING-2 후진_SOL

LEAK UPR BLOCKING 전진_SOL

LEAK UPR BLOCKING 후진_SOL

PROJECT : 유로계_압입전 LEAK TEST M/C	제 도 DRAWN	설 계 DESIGN	검 도 CHECKED	승 인 APPROVED	 (주)대한콘트롤 Daehan Control
TITLE : PLC OUTPUT Y330~Y33F CIRCUIT	OH J.H				
DATE : 2025. 06. 14	DWG NO. 400-04				